
PLANO DEL LOTE No. 12 DEL PREDIO RUSTICO DENOMINADO EL VOLANTIN, DEL MPIO. DE ARMERIA, EDO. DE COLIMA.

PROP. JUAN CARLOS HERRERA MONTES DE OCA

ESC. 1:300

Sup. 7-00-00 Has.

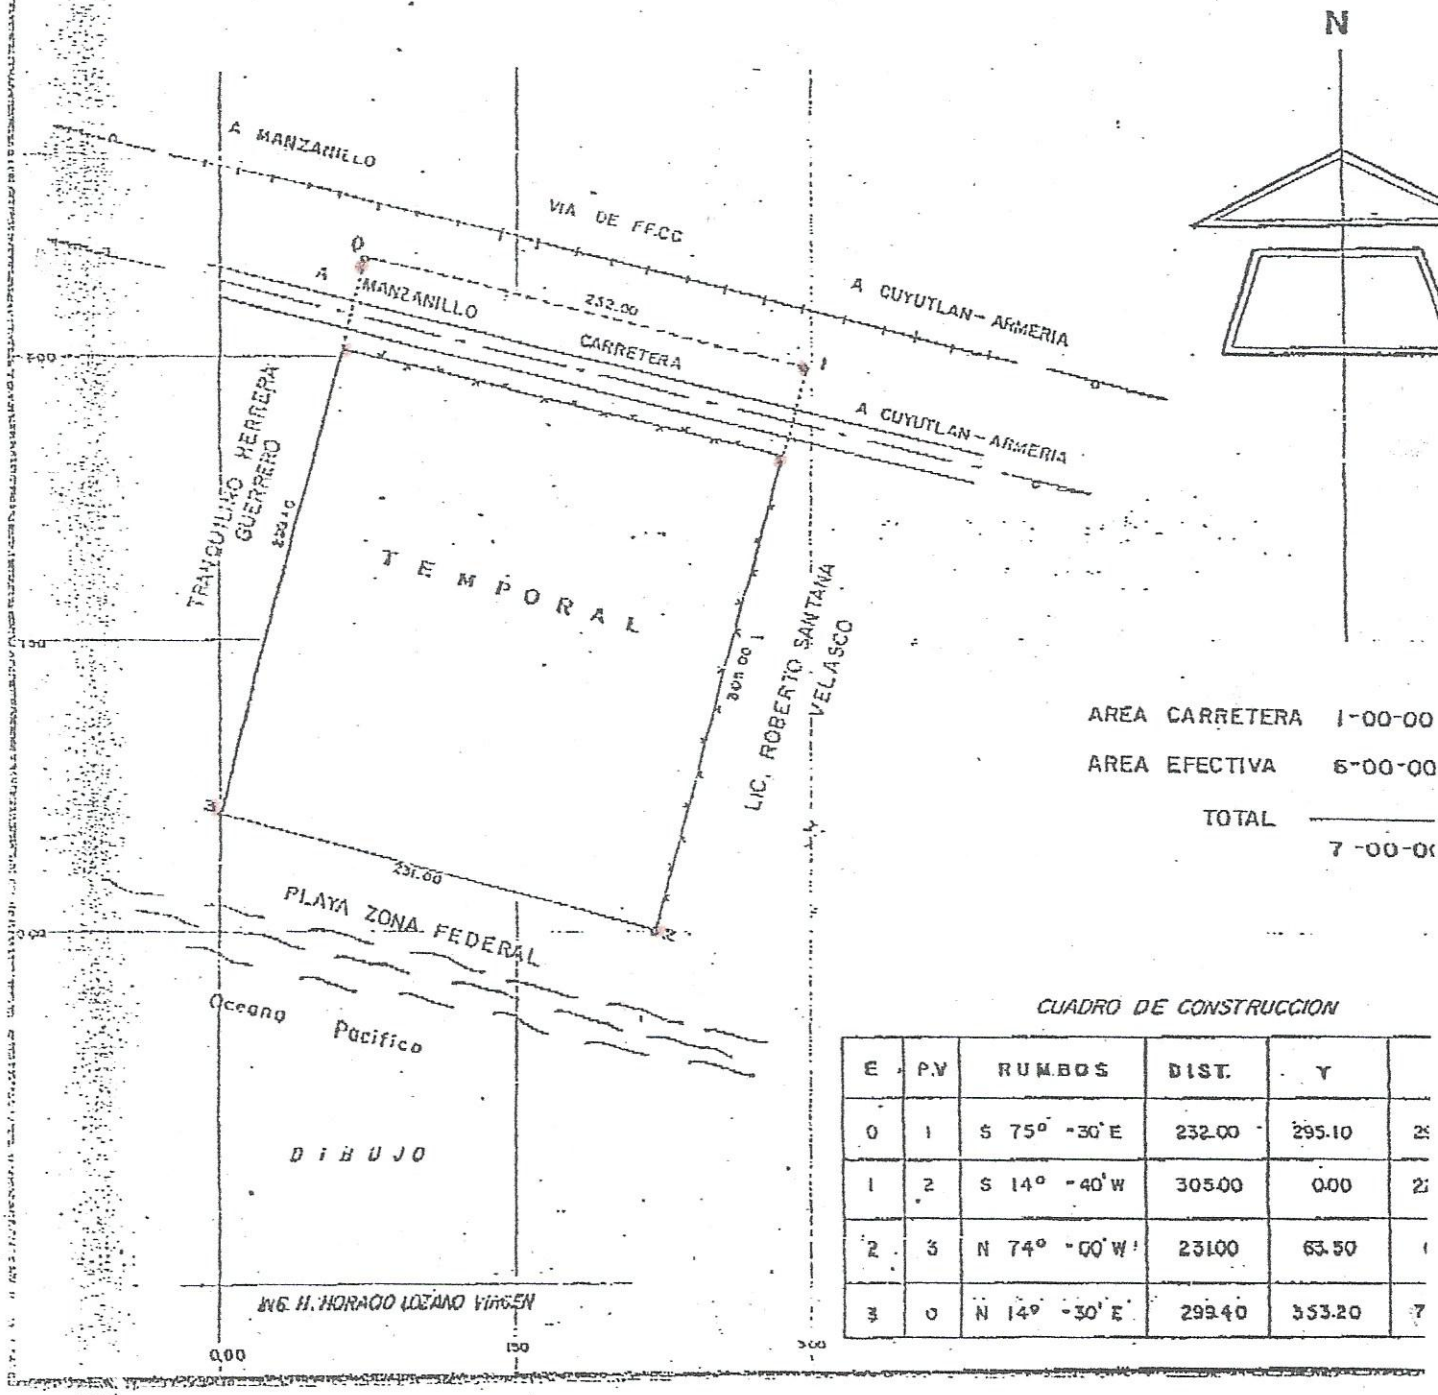

AREA CARRETERA 1-00-00

AREA EFECTIVA 6-00-00

TOTAL 7-00-00

CUADRO DE CONSTRUCCION

E	P.V	RUMBOS	DIST.	Y	
0	1	S 75° -30' E	232.00	295.10	2
1	2	S 14° -40' W	305.00	0.00	2
2	3	N 74° -00' W	231.00	63.50	
3	0	N 14° -30' E	299.40	353.20	7